

THINK SAFETY - WORK SAFELY

GENERAL NOTES:


1. DENOTES: SELF CONTAINED SMOKE ALARM COMPLYING WITH AUSTRALIAN STANDARDS. CONNECTED TO CONSUMER MAINS POWER, WITH A 9V BATTERY BACKUP.
2. DOWNSPIKE SPACING IS NOT TO EXCEED 12 METRES AVERAGE. DOWNSPIKES ARE TO BE INSTALLED WITHIN 12 METRES OF A VALLEY GUTTER WHERE IT IS NOT POSSIBLE TO LOCATE A DOWNSPIKE WITHIN 12 METRES OF THE VALLEY GUTTER AN OVERFLOW MUST BE PROVIDED IN THE GUTTER.
3. THE INSTALLATION OF REMOVABLE HINGES TO TOILET DOORS REQUIRED WHERE CLEARANCE FROM DOORWAY TO PAN IS LESS THAN 1200mm.

5,336mm

1,876mm

4,574mm

2,188mm

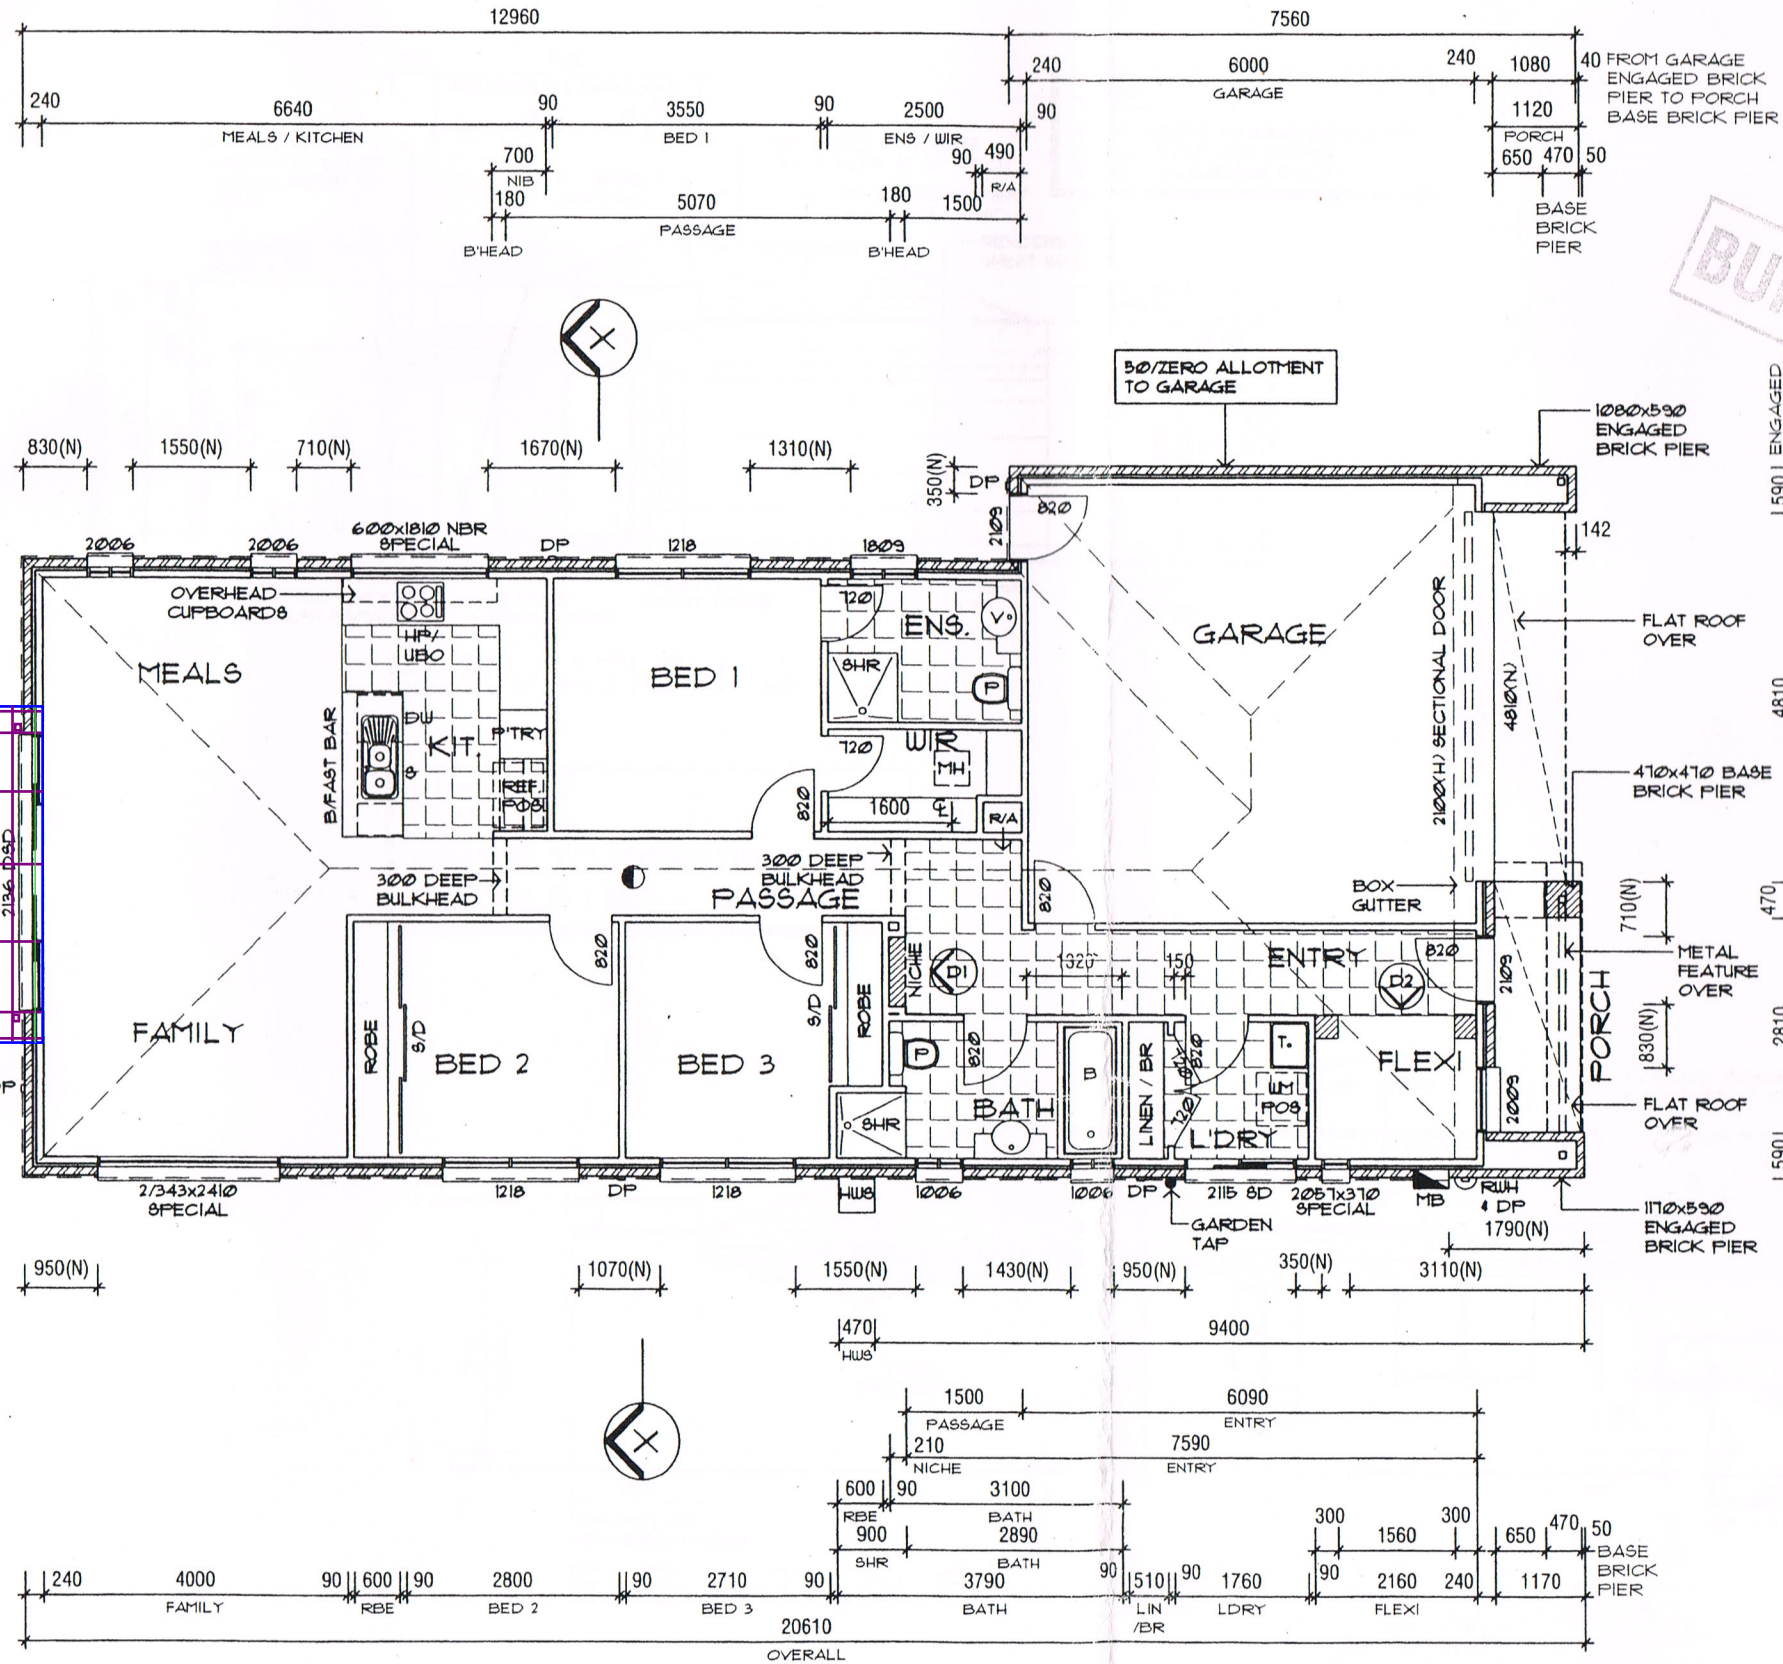

Devine
Homes

Devine Homes Pty Ltd
ACN 010 798 384
GPO FLR 88 CONVENT STREET
8TH MELBOURNE
TELEPHONE: 0699 3100, FAX: 0699 3100

DC
designedge

NATIONAL DESIGN
OFFICE

THIS IS THE PLAN
REFERRED TO IN THE
CONTRACT DATED

OWNER


OWNER

DRAWING TITLE


FLOOR PLAN

FOR: D. A. & G. V. Taylor
AT: Lot 1181 Young Street,
PAKENHAM

VIC	MODEL:	FACADE:	COLLECTION:
RH	COMO 170	STUDIO S3	(WPS)
SCALE 1:100	AREA		REVISION:
DRAWN: AW	LIVING:	26.16m2	
DATE: 22.04.10	GARAGE:	31.93m2	
JOB No: 211115	PORCH:	4.36m2	
TURN: 24.11.05	OUTDOOR LIVING:		
MAP REF: 317 G4	TOTAL:	169.05m2	
			SHEET: 01 of 10

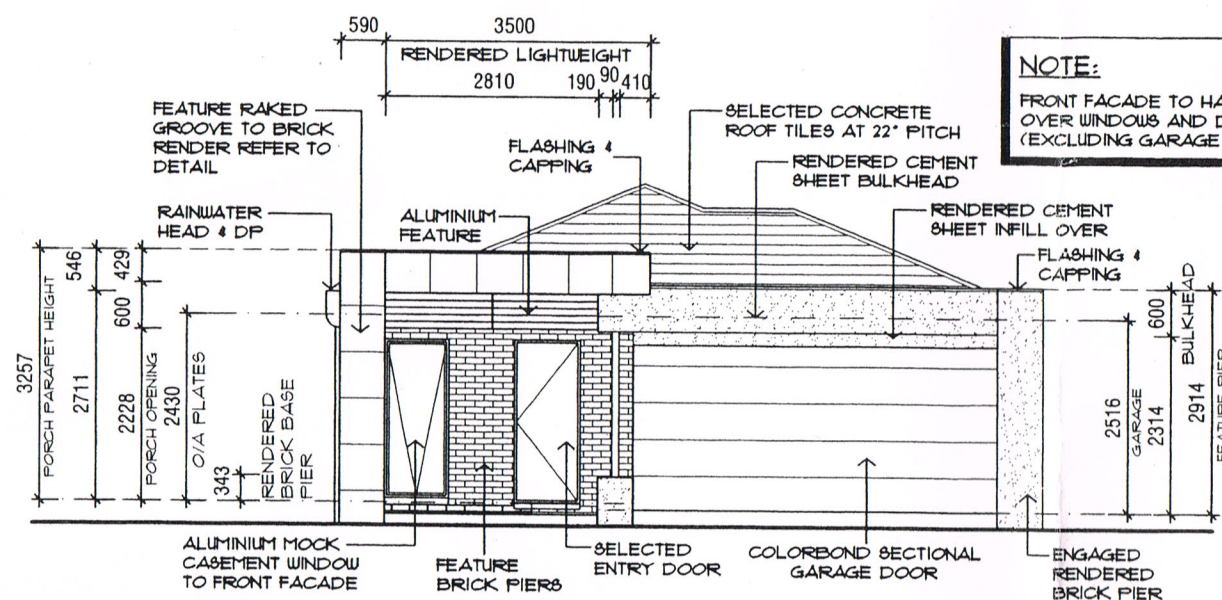


NOTE:
 FRONT FACADE TO HAVE BRICKWORK OVER WINDOWS AND DOORS (EXCLUDING GARAGE DOOR)

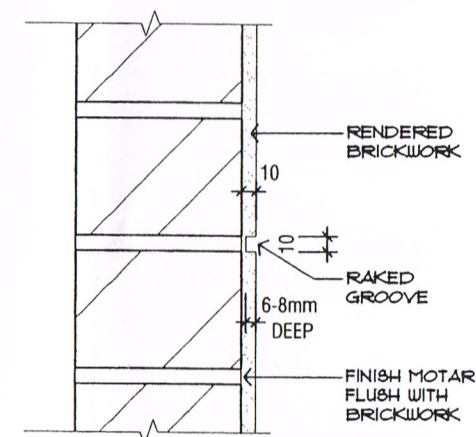

FEATURE RAKED GROOVE DETAIL
 SCALE 1:5

ELEVATION A

NOTE:
 REFER TO CONSTRUCTION DETAILS (B17 - B20)

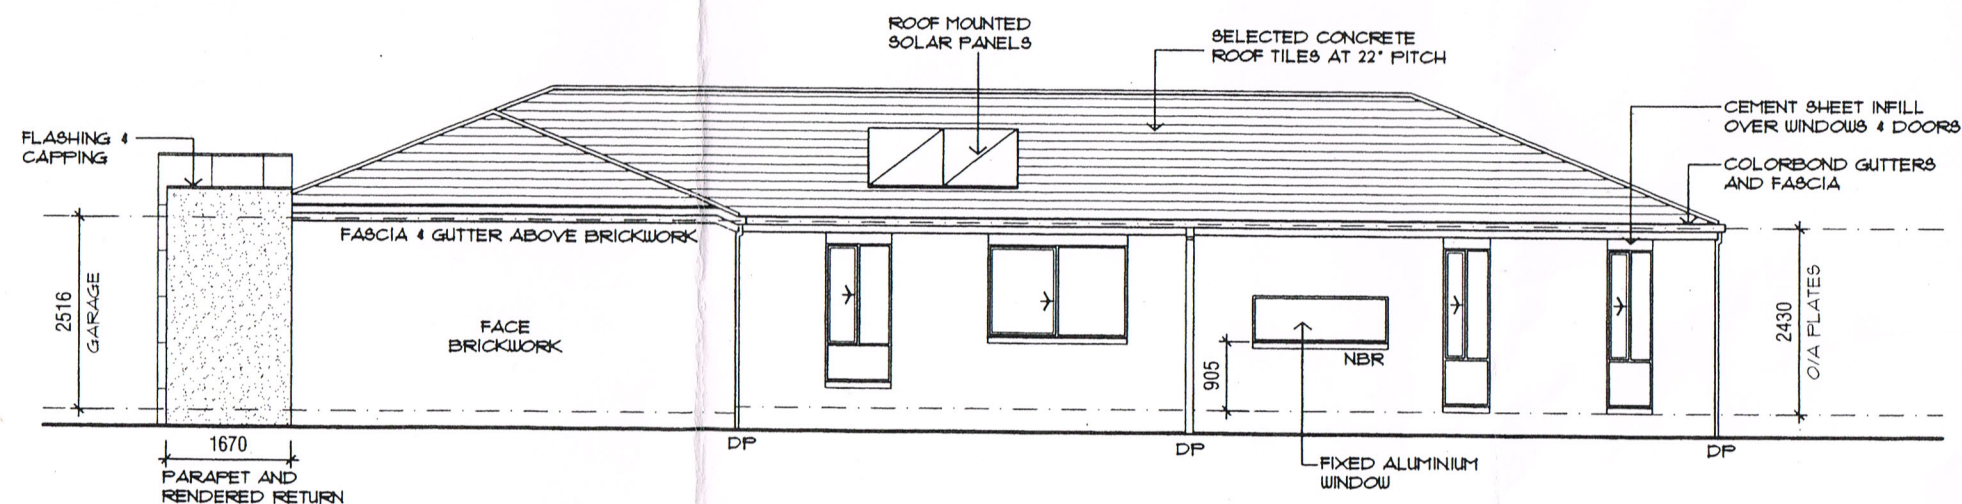

ELEVATION B

NOTE:
 BRICKWORK 5mm MIN CLEARANCE TO ALL BRICK WINDOW SILLS

NOTE:
 PROVIDE INFILLS ABOVE ALL WINDOWS AND DOORS UNLESS OTHERWISE STATED

Devine
 Homes

Devine Homes Pty Ltd
 ACN 010 198 384
 GPO FILE 88 COVENTRY STREET
 8TH FLOOR MELBOURNE
 TELEPHONE: 06 93 31000 FAX: 06 93 31000

DC
 designedge

NATIONAL DESIGN
 OFFICE

THIS IS THE PLAN REFERRED TO IN THE CONTRACT DATED

OWNER


OWNER

DRAWING TITLE


FOR: D. A. & G. V. Taylor
 AT: Lot 1181 Young Street,
 PAKENHAM

ELEVATIONS

VIC	MODEL: RH	COMO 170	FACADE: STUDIO 53	COLLECTION: (WFS)
SCALE 1:100	AREA			REVISION:
DRAWN: AW	LIVING:	126.16m ²		
DATE: 22.04.10	GARAGE:	37.93m ²		
JOB No: 211115	PORCH:	4.36m ²		
PREP: 24.11.09	OUTDOOR LIVING:			
MAP REF: 317 G4	TOTAL:	169.05m ²		SHEET: 02 OF 10

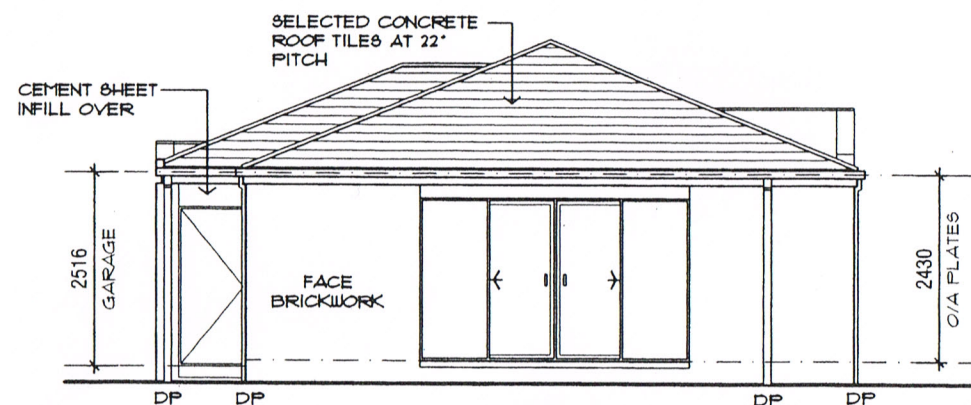


ELEVATION C

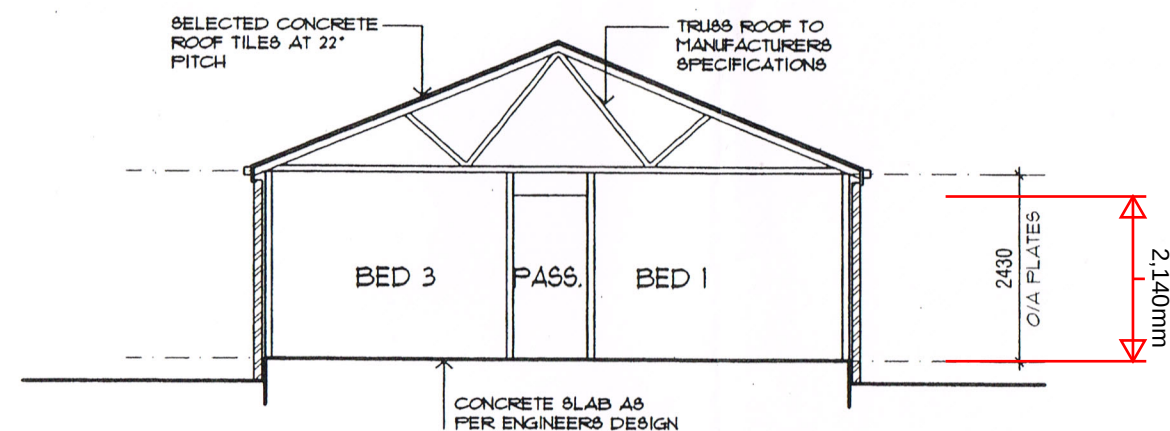

FOR SOIL CLASSIFICATION REFER TO ENG'S SOIL REPORT

SECTION X - X

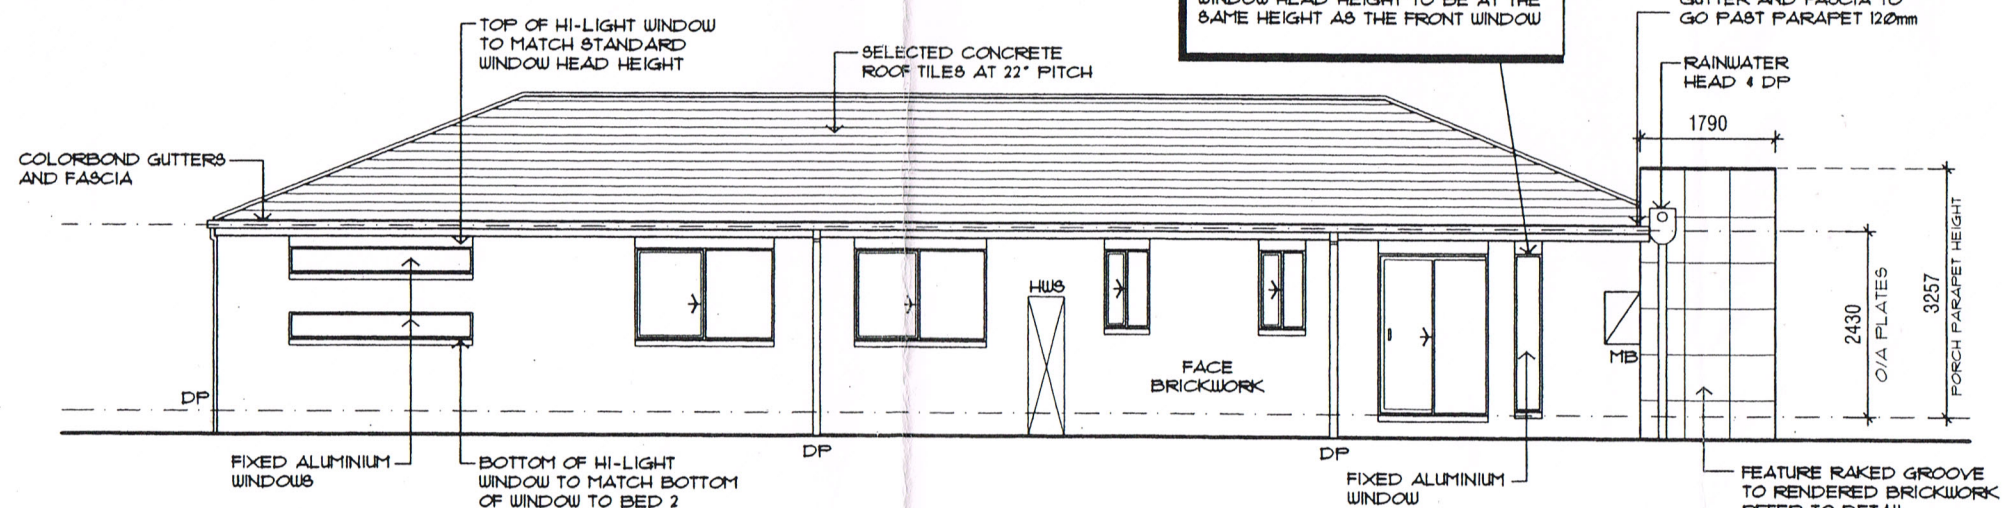

ELEVATION D

NOTE:
BRICKWORK 5mm MIN
CLEARANCE TO ALL
BRICK WINDOW SILLS

NOTE:
PROVIDE INFILLS ABOVE ALL
WINDOWS AND DOORS UNLESS
OTHERWISE STATED

Devine
Homes

Devine Homes Pty Ltd
ACN 010 798 384
GND FLR 83 COVENTRY STREET
6TH FLOOR
TELEPHONE: 06 93 3100 FAX: 06 93 3100

DC
designedge

NATIONAL DESIGN
OFFICE

THIS IS THE PLAN
REFERRED TO IN THE
CONTRACT DATED

OWNER


OWNER

DRAWING TITLE ELEVATIONS & SECTION

FOR: D. A. & G. V. Taylor
AT: Lot 1181 Young Street,
PAKENHAM


VIC	MODEL: RH COMO 110	FACADE: STUDIO S3	COLLECTION: (WPS)
SCALE 1:100	AREA		REVISION:
DRAWN: AW	LIVING:	126.76m2	
DATE: 22.04.10	GARAGE:	37.93m2	
JOB No: 211115	PORCH:	4.36m2	
REV: 24.11.09	OUTDOOR LIVING:		
MAP REF: 317 G4	TOTAL:	169.05m2	SHEET: 03 OF 10

EVAP COOLING LEGEND

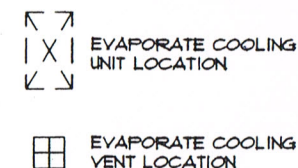

ELECTRICAL LEGEND

- GPO'S**
- ▲ SINGLE GPO
 - ▲ DOUBLE GPO
 - △ EXTERNAL WEATHER PROOF SINGLE GPO
 - △ EXTERNAL WEATHER PROOF DOUBLE GPO
- HEIGHTS OF GPO'S**
- GENERAL - 200mm ABOVE FFL.
 - KITCHEN - 1000mm ABOVE FFL.
 - FRIDGE LOCATION - 1100mm ABOVE FFL.
 - BATH/EN'S - 1100mm ABOVE FFL.
 - LAUNDRY - 1100mm ABOVE FFL.
 - EXTERNAL W/PROOF - 600mm ABOVE FFL.
 - GARAGE GENERAL - 1100mm ABOVE FFL.
 - 8.G.P.O. 600mm ABOVE FFL. FOR DISHWASHER SPACE
 - 8.G.P.O. 1600mm ABOVE FFL. FOR RANGEHOOD AND MICROWAVE SPACE IN WALL OVEN TOWER
 - GARAGE REMOTE ROLLER DOOR- LOCATE ON WALL 1800 AFFL
 - GARAGE REMOTE PANEL DOOR - LOCATE ON CEILING 3300mm FROM DOOR OPENING LINTEL 4 200mm OFF DOOR CENTRE.
- HEIGHTS OF LIGHT SWITCHES**
- LIGHT SWITCH - 1100mm ABOVE FFL.
 - TELEVISION POINT - 200mm ABOVE FFL.
 - LIGHT SWITCH FOR HEATING UNIT 1500mm ABOVE FFL. WITHIN CLOSE PROXIMITY OF MANHOLE
 - SEALED EXHAUST FAN
 - LOW VOLTAGE DOWNLIGHT
 - CEILING MOUNTED LIGHT
 - WALL MOUNTED LIGHT - 1800mm AFFL
 - TELEPHONE POINT - 1200mm AFFL
 - TELEPHONE POINT - 200mm AFFL
 - METER BOX
 - SMOKE DETECTOR
 - ROOF MOUNTED SOLAR PANEL
 - DUCTED HEATING VENT LOCATION
 - MAN HOLE
 - R/A RETURN AIR FOR DUCTED HEATING
 - DUCTED HEATING UNIT TO BE LOCATED IN CEILING ABOVE PASSAGE
- PROVIDE POWER POINT, GAS POINT & LIGHT POINT IN CEILING FOR DUCTED HEATING UNIT

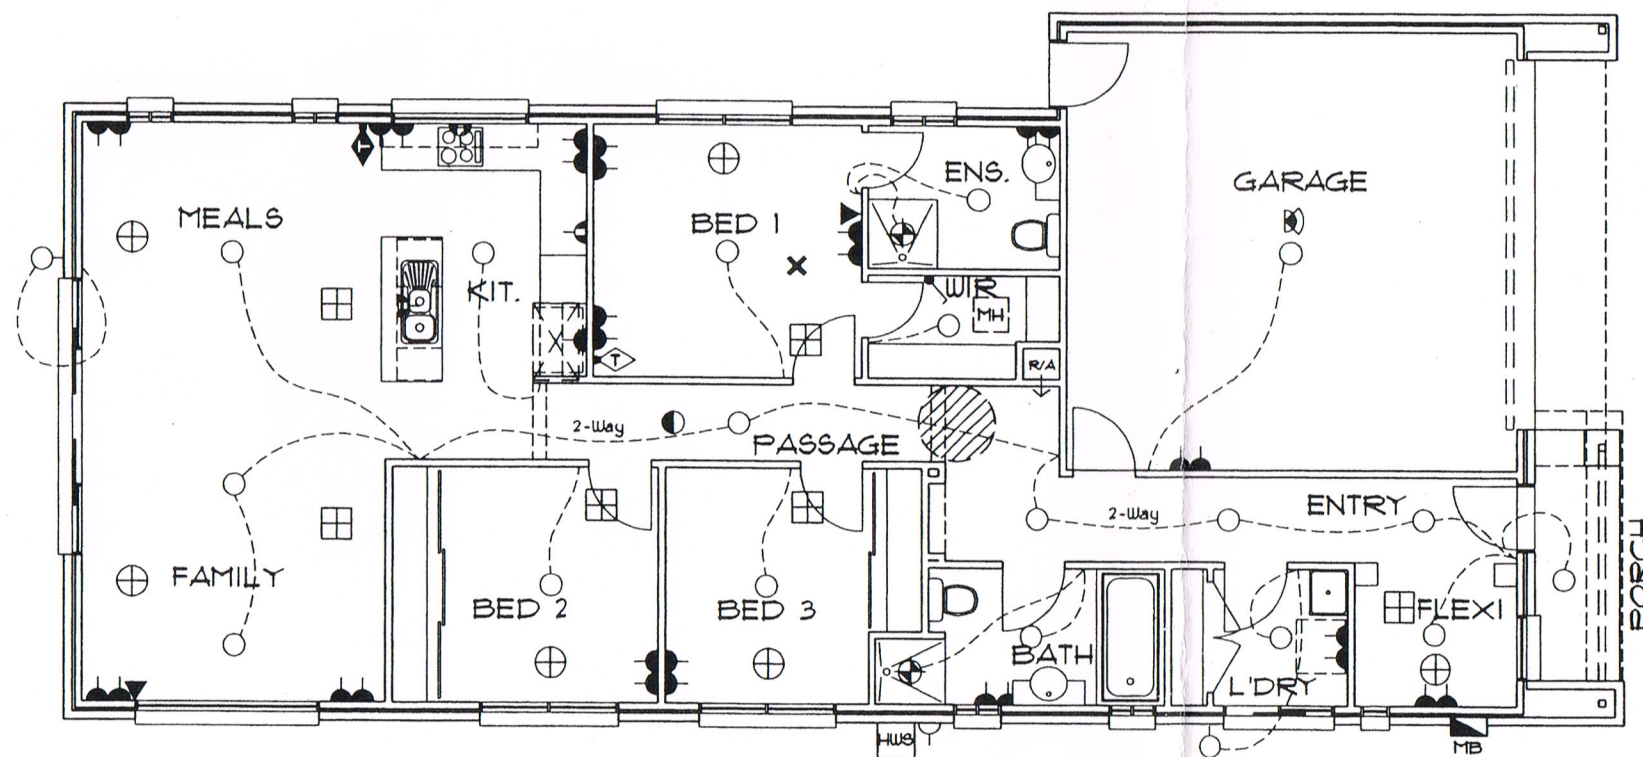

Devine
Homes

Devine Homes Pty Ltd
ACN 010 198 384
GPO FLR 88 COVENTRY STREET
8TH MELBOURNE
TELEPHONE: 0693 3100 FAX: 0693 3100

DC
designedge

NATIONAL DESIGN
OFFICE

THIS IS THE PLAN
REFERRED TO IN THE
CONTRACT DATED

OWNER

OWNER


DRAWING TITLE

ELECTRICAL PLAN


FOR: D. A. & G. V. Taylor

AT: Lot 1181 Young Street,
PAKENHAM


VIC	MODEL: RH COMO 110	FACADE: STUDIO S3	COLLECTION: (WPS)
SCALE 1:100	AREA		REVISION:
DRAWN: AW	LIVING:	126.76m ²	
DATE: 22.04.10	GARAGE:	37.93m ²	
JOB No: 211115	PORCH:	436m ²	
PREP: 24.11.09	OUTDOOR LIVING:		
MAP REF: 317 G4	TOTAL:	169.05m ²	SHEET: 04 OF 10

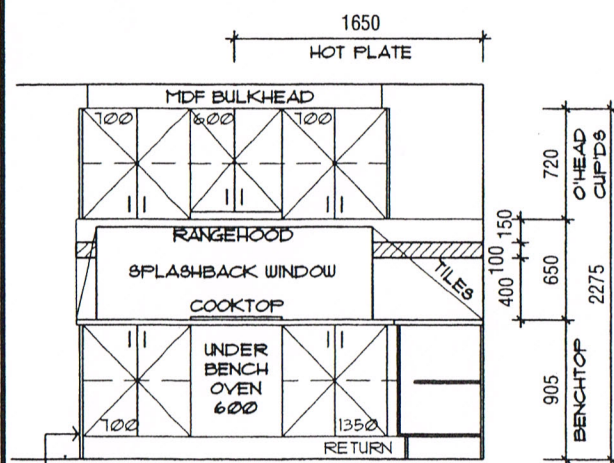


ELEVATION 1

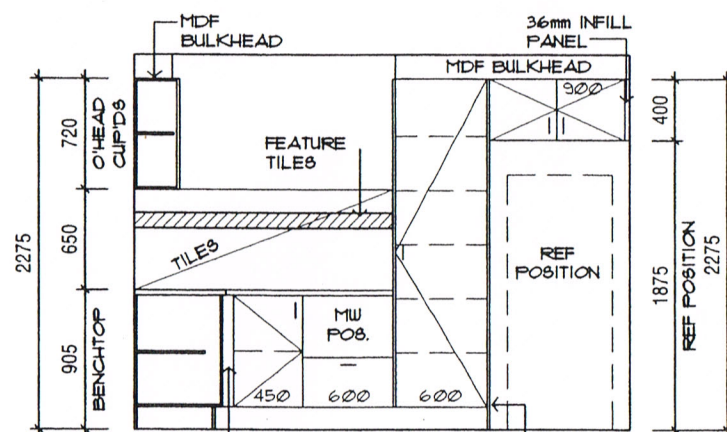


ELEVATION 2

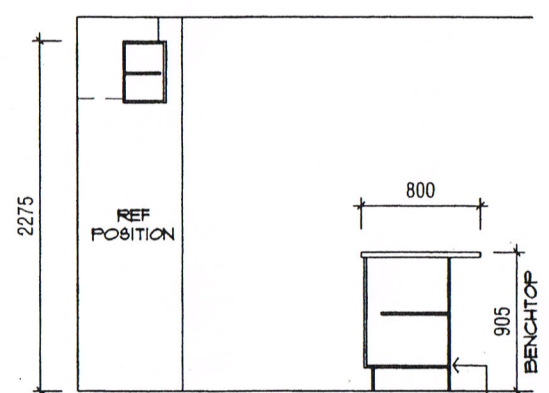

ELEVATION 3

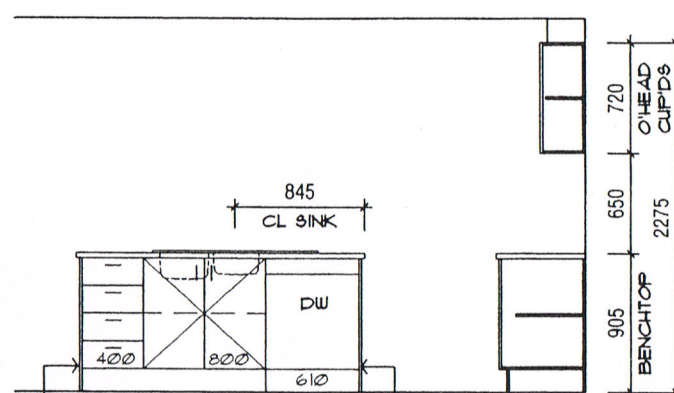


ELEVATION 4

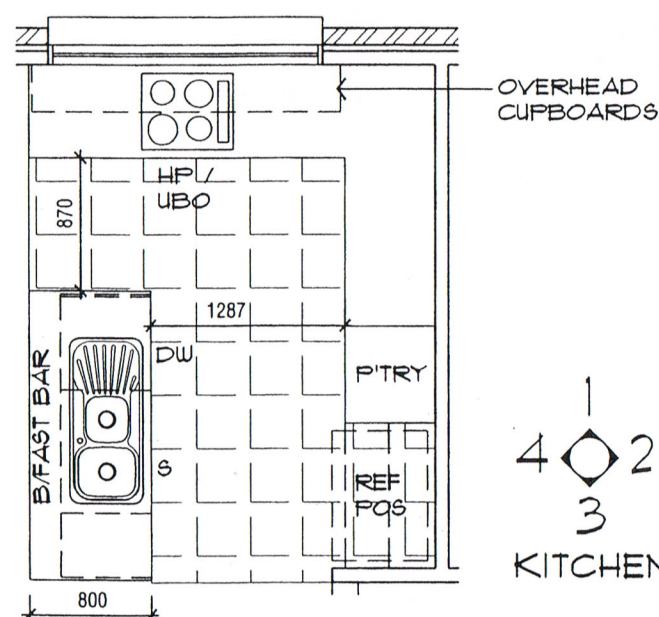


KITCHEN FLOOR PLAN

KITCHEN NOTES


COLD WATER POINT & POWER POINT WITH JUNCTION PIECE TO SINK TRAP (INC. PRESSURE RESTRICTING VALVE) ONLY FOR OWNERS FUTURE DISHWASHER

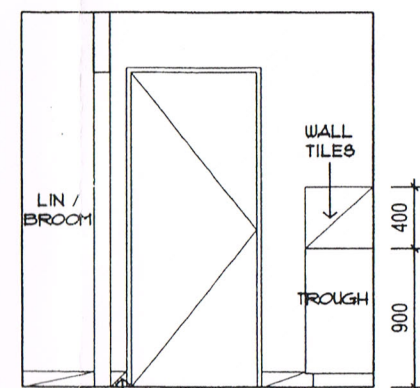

ELEVATION 1

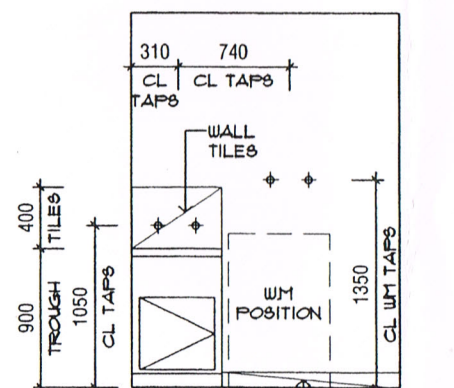

ELEVATION 2

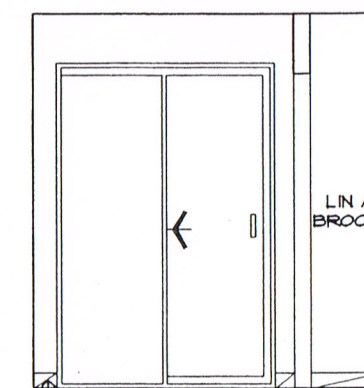


ELEVATION 3




LAUNDRY FLOOR PLAN

NOTE:
SKIRTING TILES TO LAUNDRY TO BE SAME AS FLOOR TILES.
METAL TILE TRIMS TO ALL DOOR OPENINGS.


1
4 2
3
L'DRY

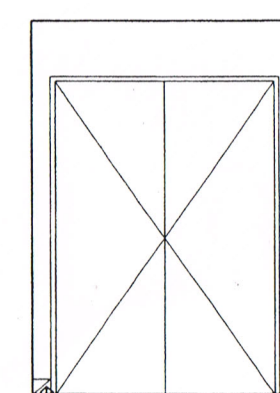

ELEVATION 4

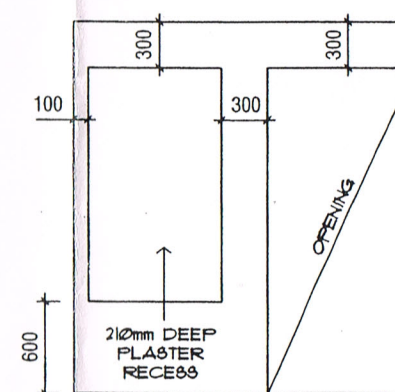

DETAIL 1

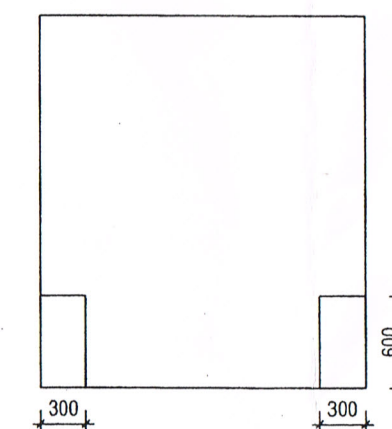

DETAIL 2

INTERNAL DETAILS

Devine
Homes

Devine Homes Pty Ltd
ACN 010 198 384,
6RD FLD, 88 COVENTRY STREET,
8TH, MELBOURNE
TELEPHONE: 06 99 3100, FAX: 06 99 3100

DC
designedge

NATIONAL DESIGN
OFFICE

THIS IS THE PLAN
REFERRED TO IN THE
CONTRACT DATED

OWNER

OWNER

DRAWING TITLE

WET AREA DETAILS

FOR: D. A. & G. V. Taylor

AT: Lot 1181 Young Street,
PAKENHAM

VIC MODEL:
RH COMO 170

FACADE:
STUDIO S3

COLLECTION:
(WFS)

SCALE 1:50

DRAWN: AW

DATE: 22.04.10

JOB No: 211115

PREV: 24.11.09

MAP REF: 317 G4

AREA

LIVING:

GARAGE:

PORCH:

OUTDOOR LIVING:

TOTAL:

126.76m2






37.93m2

4.36m2

169.05m2

REVISION:





SHEET: 05 OF 10

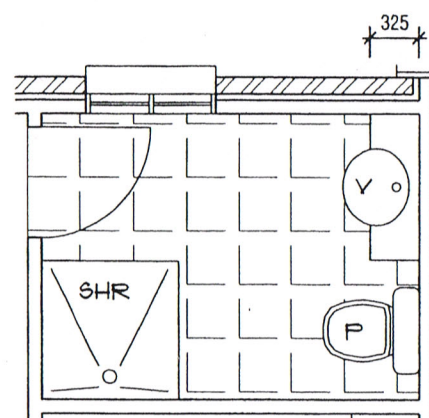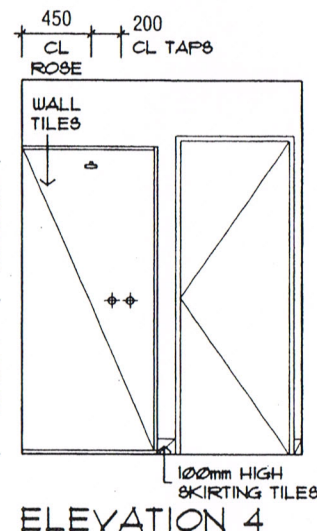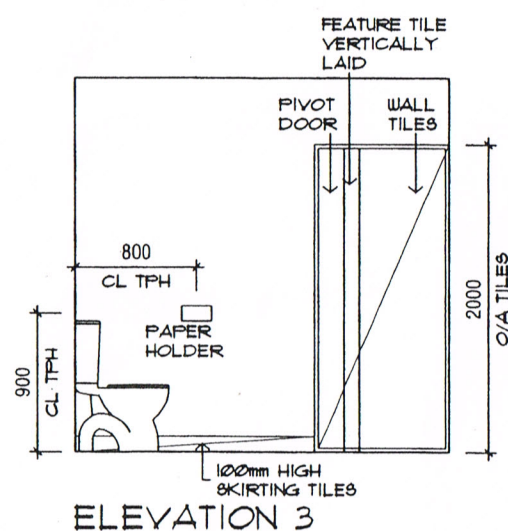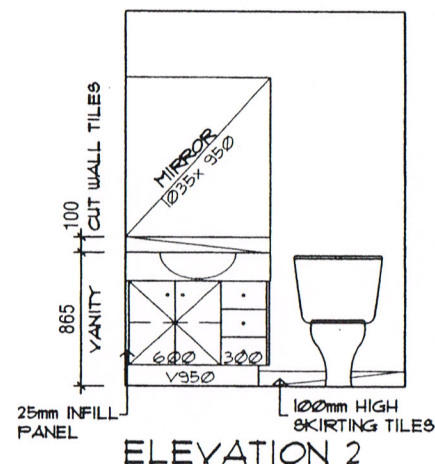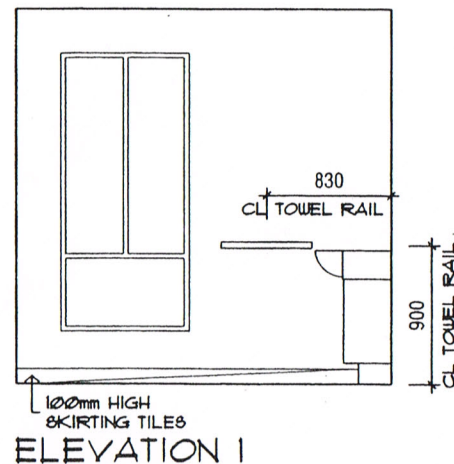

4 1 2
3
ENSUITE


NOTE:
SKIRTING TILES TO ENSUITE TO BE SAME AS FLOOR TILES.
METAL TILE TRIMS TO ALL DOOR OPENINGS.

ENSUITE FLOOR PLAN

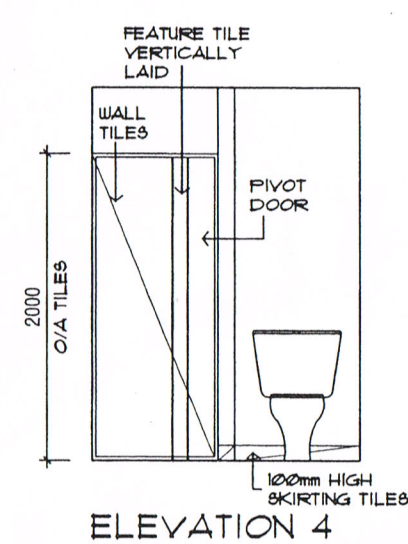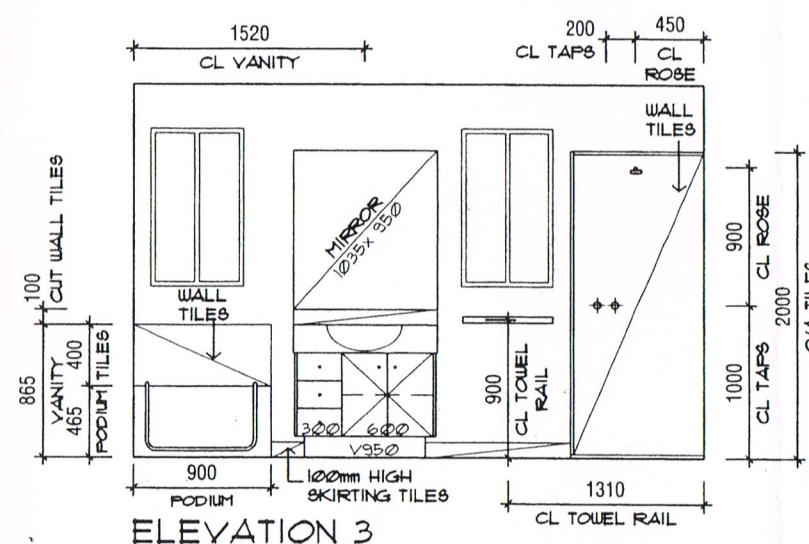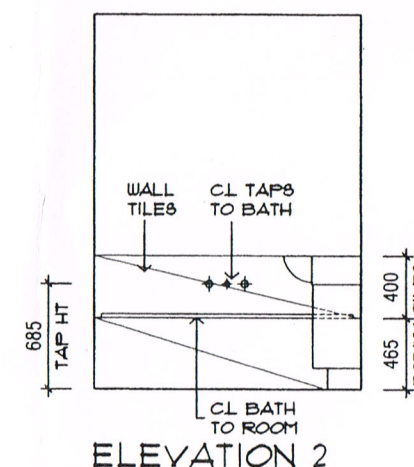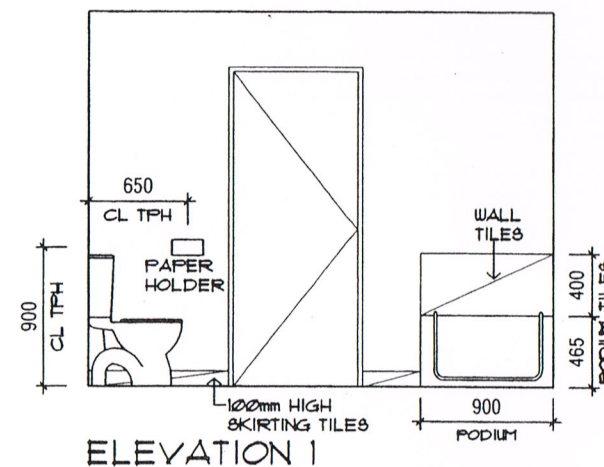

NOTE:
SKIRTING TILES TO BATHROOM TO BE SAME AS FLOOR TILES.
METAL TILE TRIMS TO ALL DOOR OPENINGS.

4 1 2
3
BATHROOM

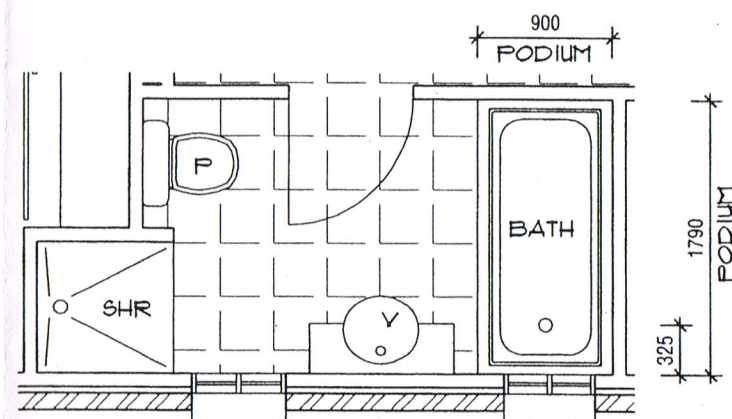

BATHROOM FLOOR PLAN

SHEET:

THINK SAFETY - WORK SAFELY

LANDSCAPING NOTE:

LANDSCAPING LAYOUT PROVIDED IS INDICATIVE ONLY, AND SUBJECT TO CHANGES AT THE DISCRETION OF THE LANDSCAPER & MAY VARY TO BEST SUIT SITE CONDITIONS

(VACANT LAND)
(AS @ 07/04/10)

9'00'00"
10.50m

CLOTHESLINE FROM
STANDARD BUILDERS
RANGE

CHILDREN'S PLAY AREA
WITH SOFTFALL MULCH AND
JARRAH EDGING.

NCA ZONE 55

LOT 1181
347m²
PROPOSED
RESIDENCE

LOT 1182
(VACANT LAND)
(AS @ 07/04/10)

LOT 1180
(VACANT LAND)
(AS @ 07/04/10)

GARAGE

189'00'00"
10.50m

Light
Pole

Existing
Crossover

Concrete Kerb
& Channe.

YOUNG STREET

NOTE:
SITE SCALE 1:200

LEGEND:



CONCRETE



HINGED GATE



LETTER BOX WITH
STREET NUMBER



SELECTED HARD FINISH




JARRAH EDGING TO CHILDRENS
PLAY AREA/ GARDEN BEDS

PROPOSED 1800mm HIGH CAPPED
TIMBER PALING FENCE



GARDEN BED

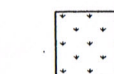

INSTANT TURF



SOFTFALL MULCH

Devine
Homes

Devine Homes Pty Ltd
ACN 010 198 384
GRD FLR 88 COVENTRY STREET,
8TH MELBOURNE
TELEPHONE: 06 99 3100. FAX: 06 99 3100

DC
designedge

NATIONAL DESIGN
OFFICE

THIS IS THE PLAN
REFERRED TO IN THE
CONTRACT DATED

OWNER

OWNER

DRAWING TITLE

LANDSCAPE PLAN

FOR: D. A. & G. V. Taylor

AT: Lot 1181 Young Street,
PAKENHAM

VIC MODEL:
RH COMO 170

FACADE:
STUDIO S3

COLLECTION:
(WPS)

SCALE 1:200

AREA

DRAIN: AU

LIVING:

126.76m²

DATE: 22.04.10

GARAGE:

37.93m²

JOB No: 211115

PORCH:

4.36m²

PREV: 24.11.09

OUTDOOR LIVING:

MAP REF: 311 G4

TOTAL:

169.05m²

SHEET: 10 OF 10